




12/23/2022 10:56:16 AM BIM 360/2/15 Bili Shanghai Headquarters/15 Bili SH HQ N3-4 Copyright © 2021 Ennead Architects, LLP

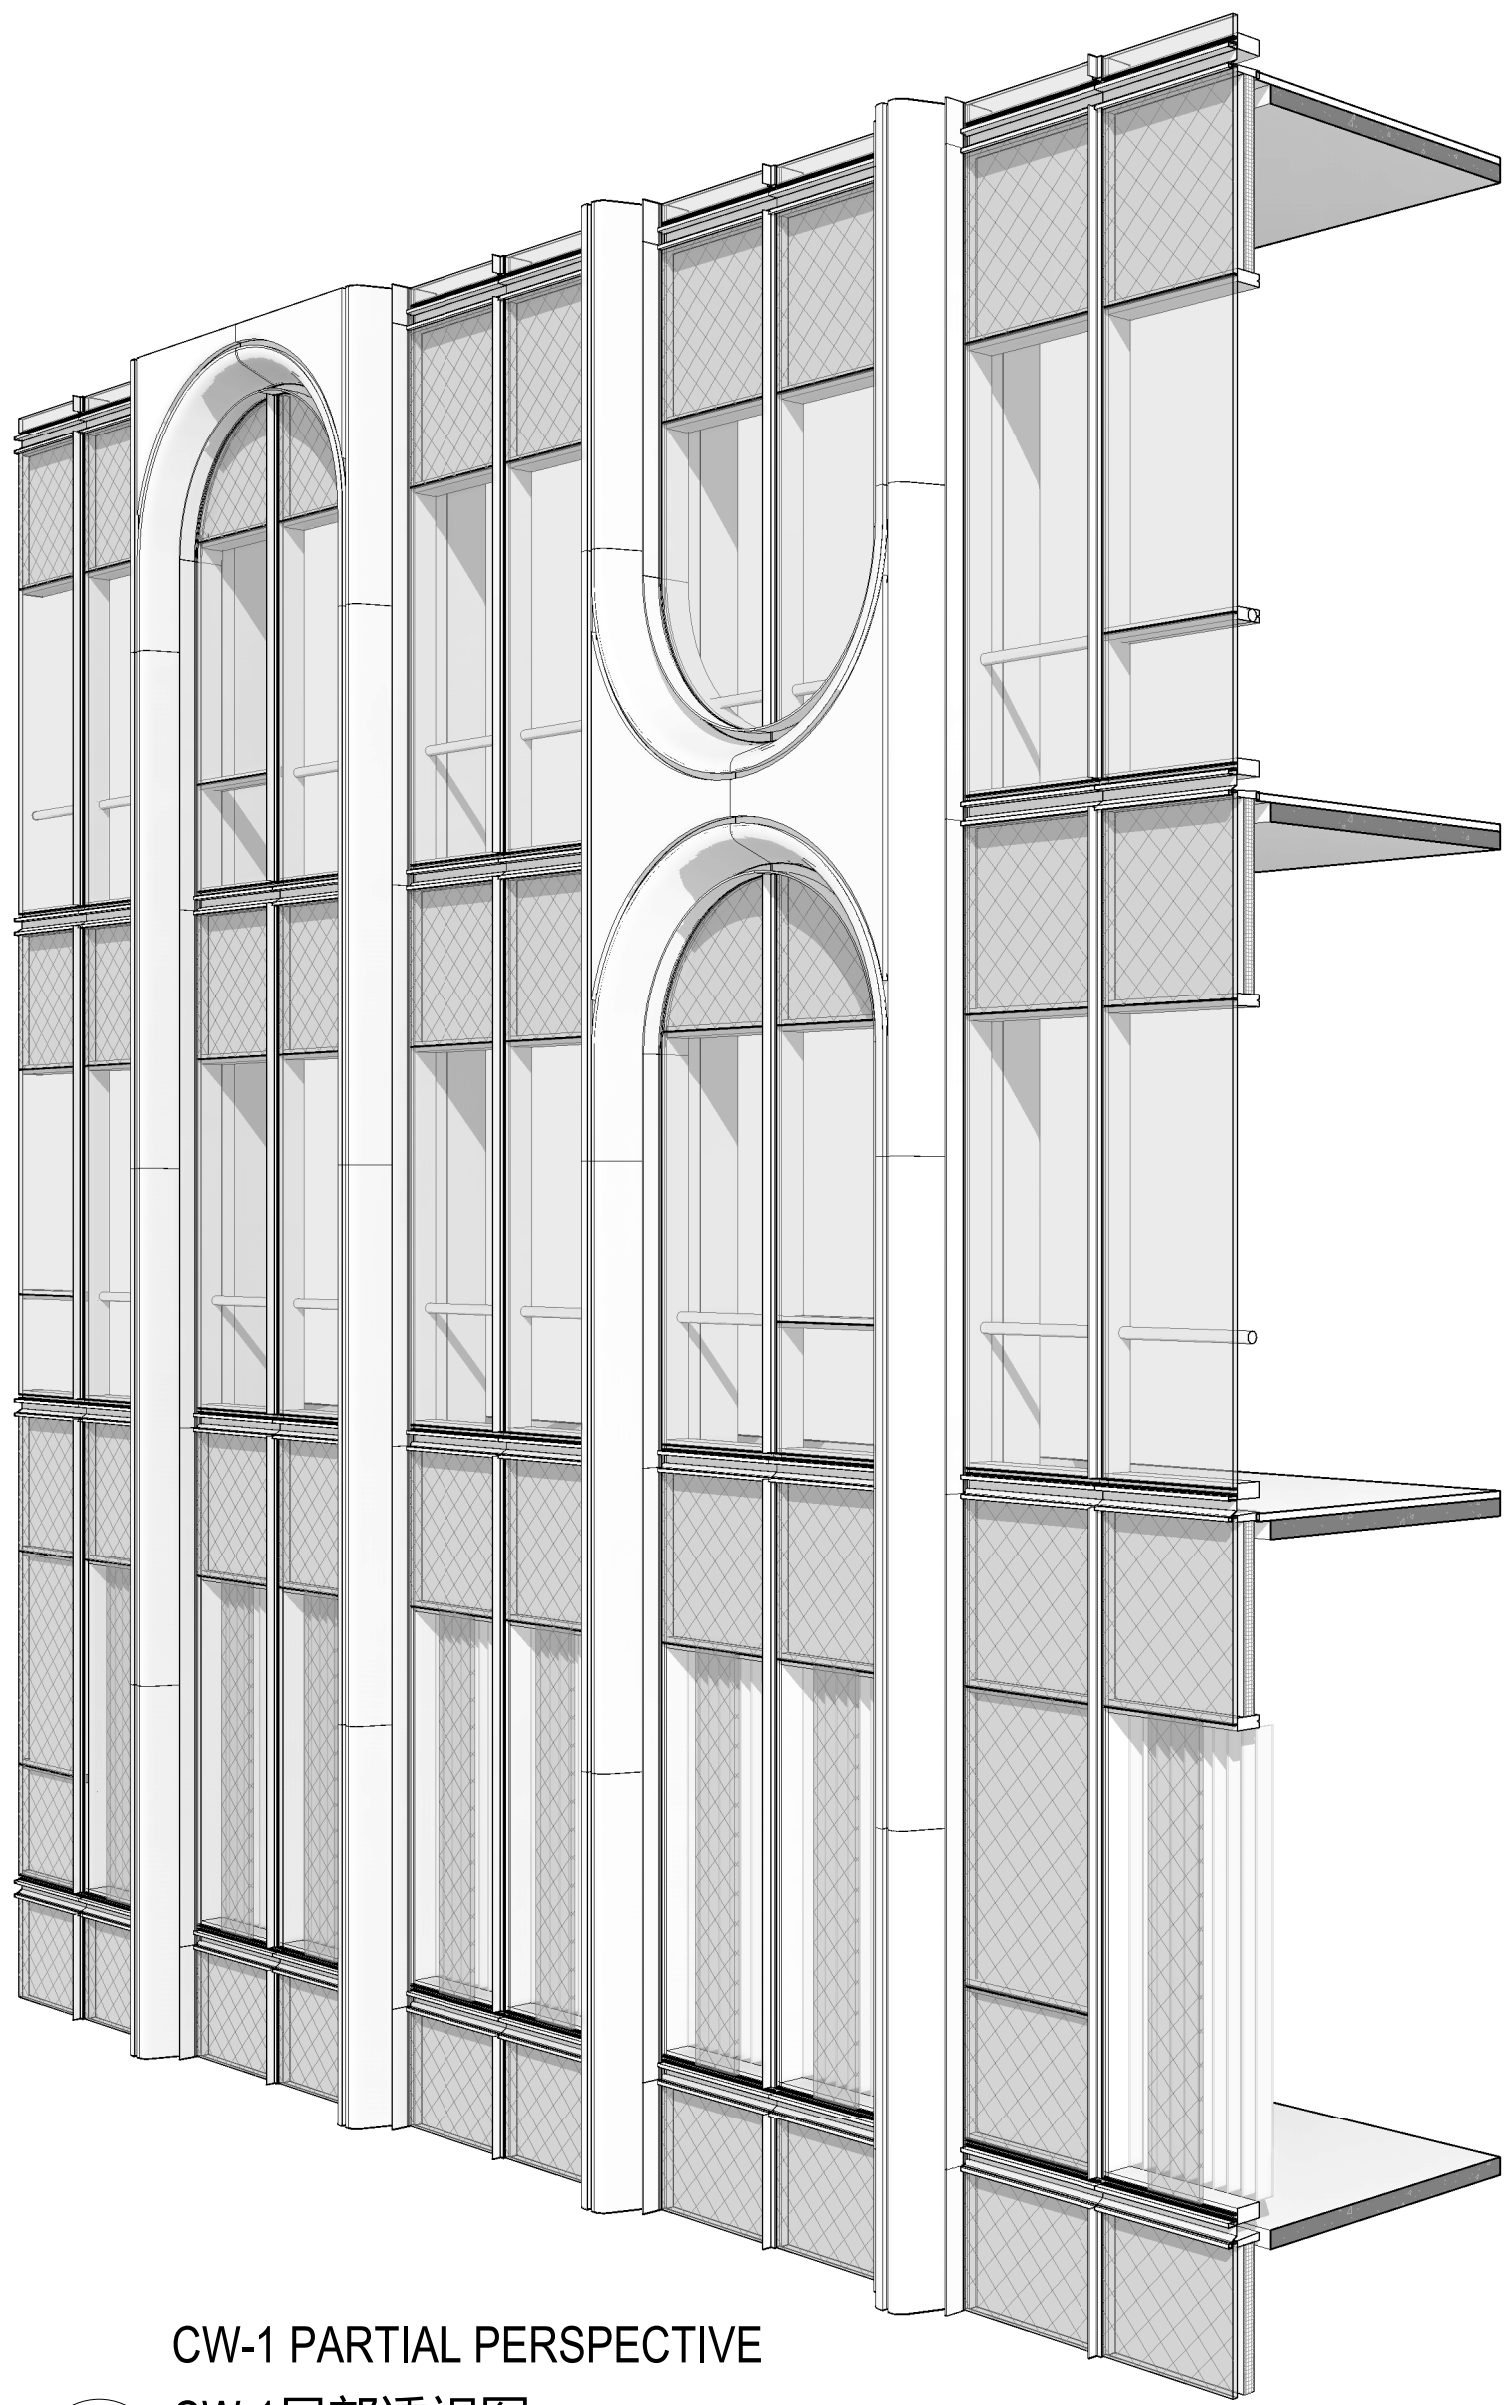


CW-1 PARTIAL PERSPECTIVE
CW-1局部透视图

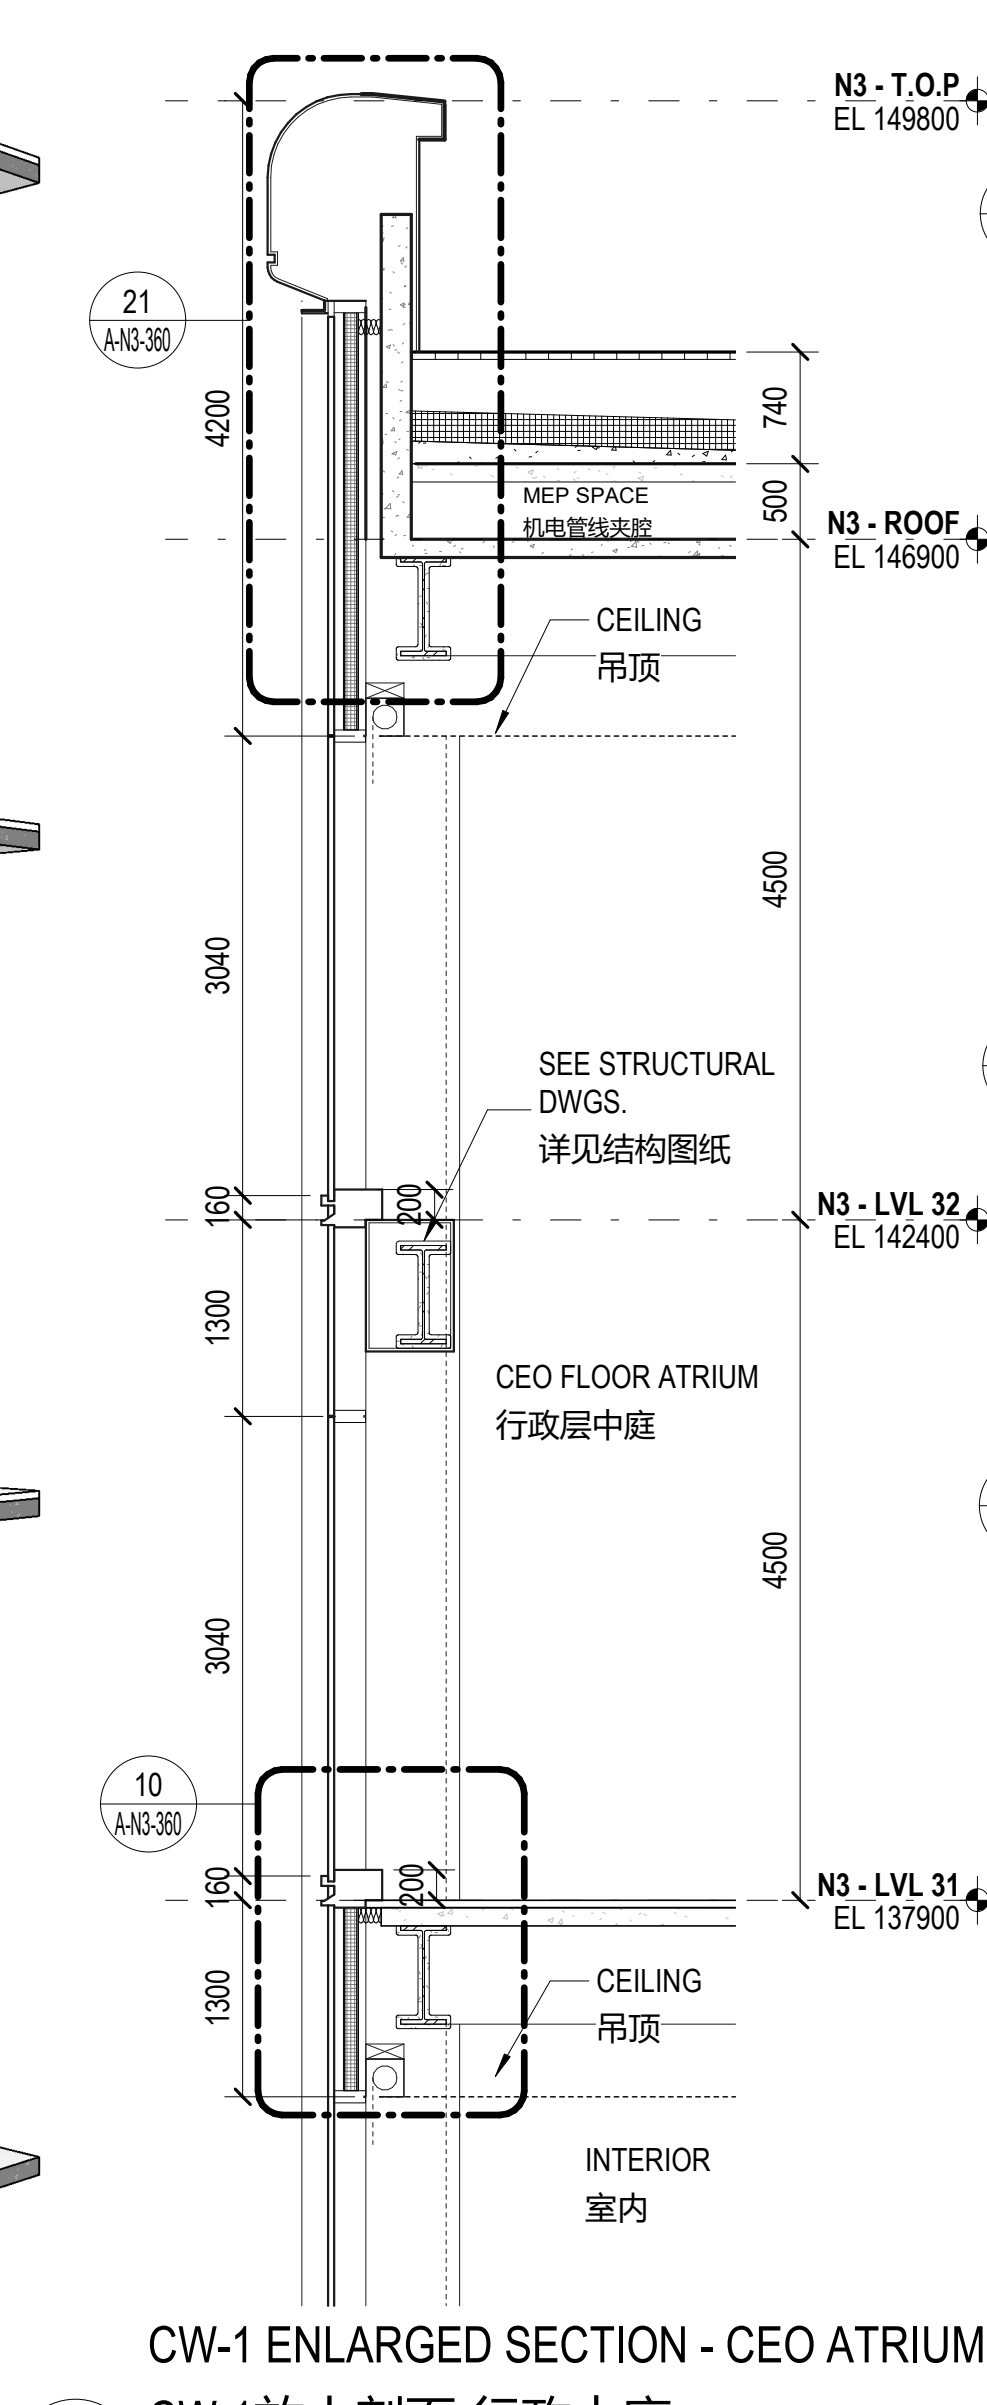


CW-1 ENLARGED SECTION - CEO ATRIUM
CW-1放大剖面-行政中庭

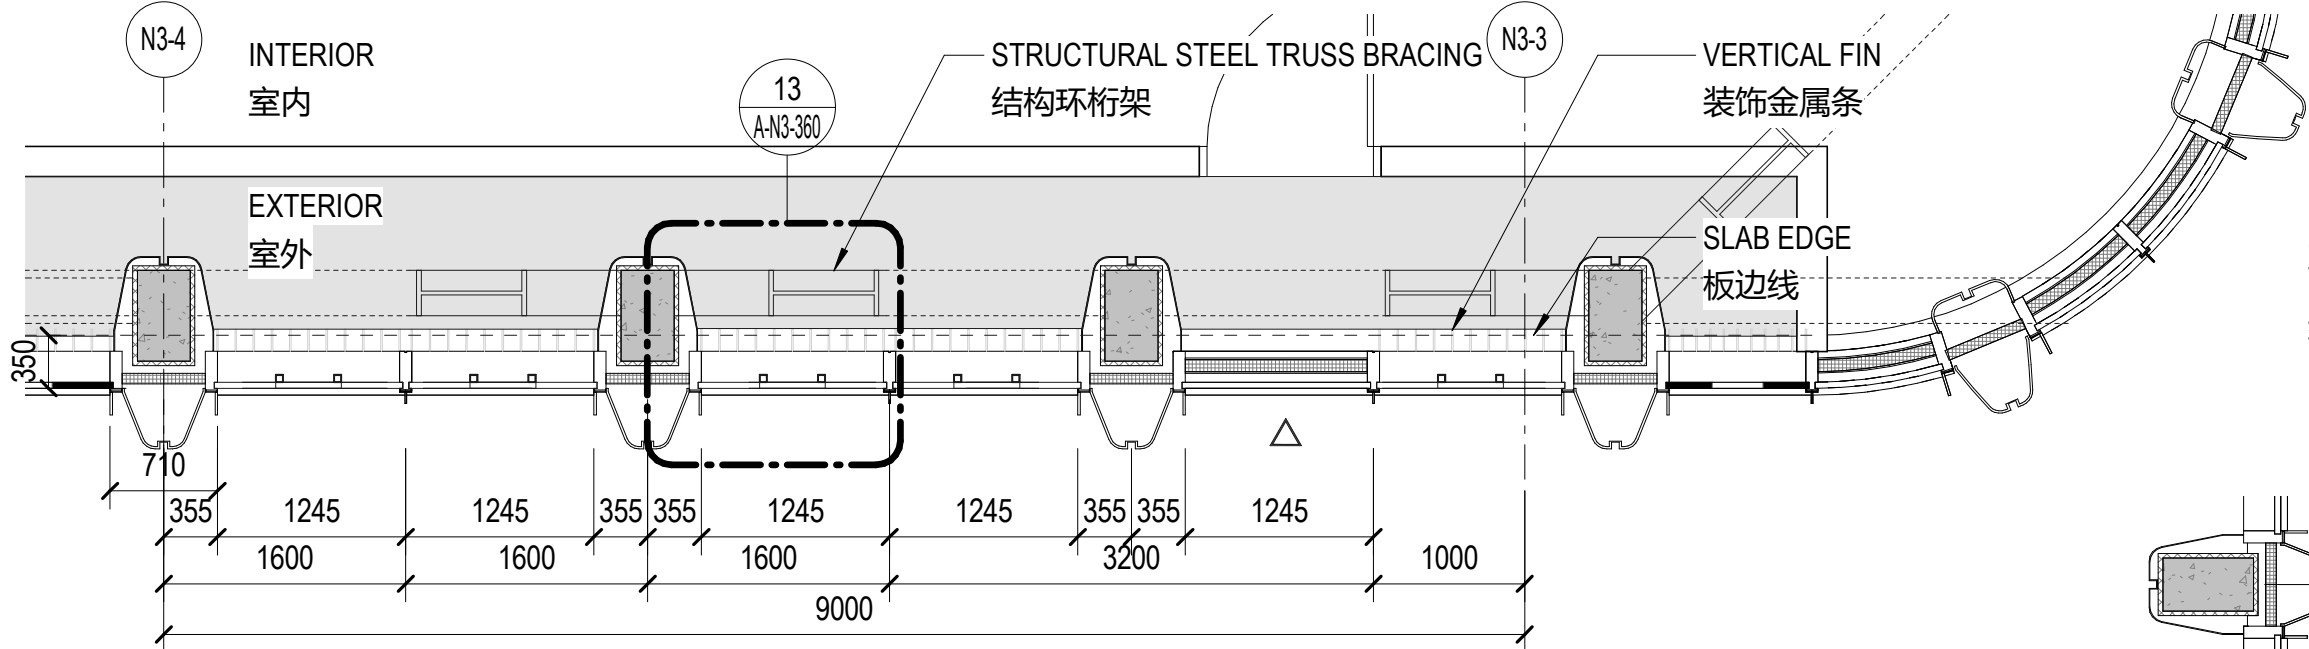


CW-1 ENLARGED PLAN - AT REFUGE FL.
CW-1 放大平面-避难层

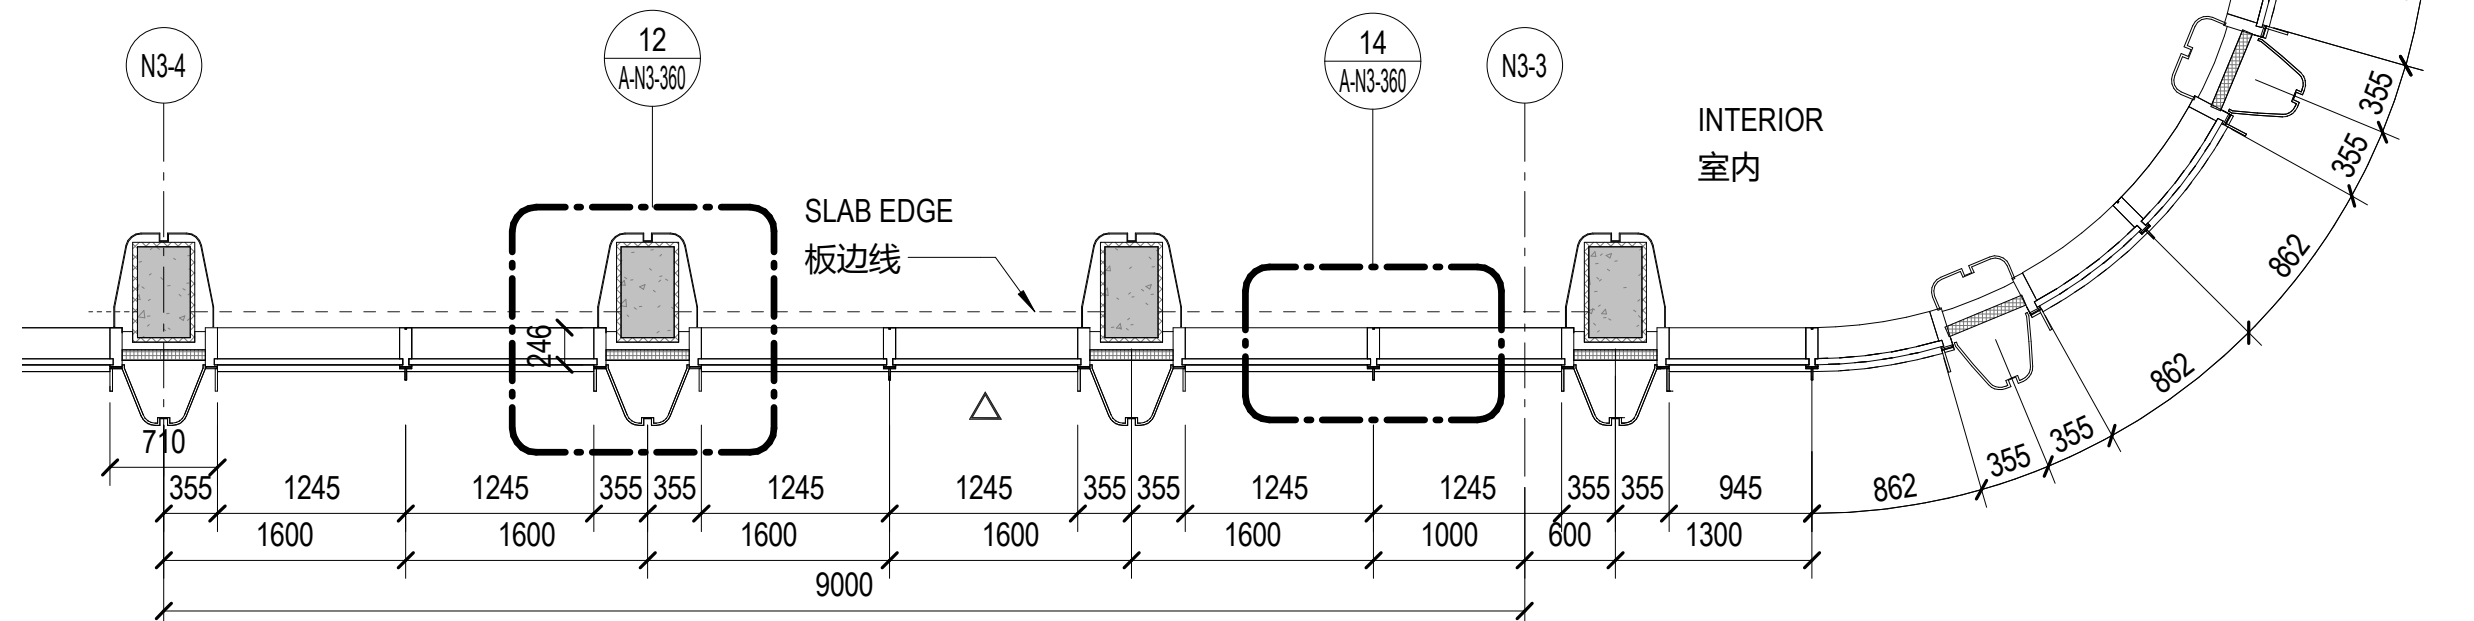


CW-1 ENLARGED PLAN - TYP.
CW-1 放大平面-标准层

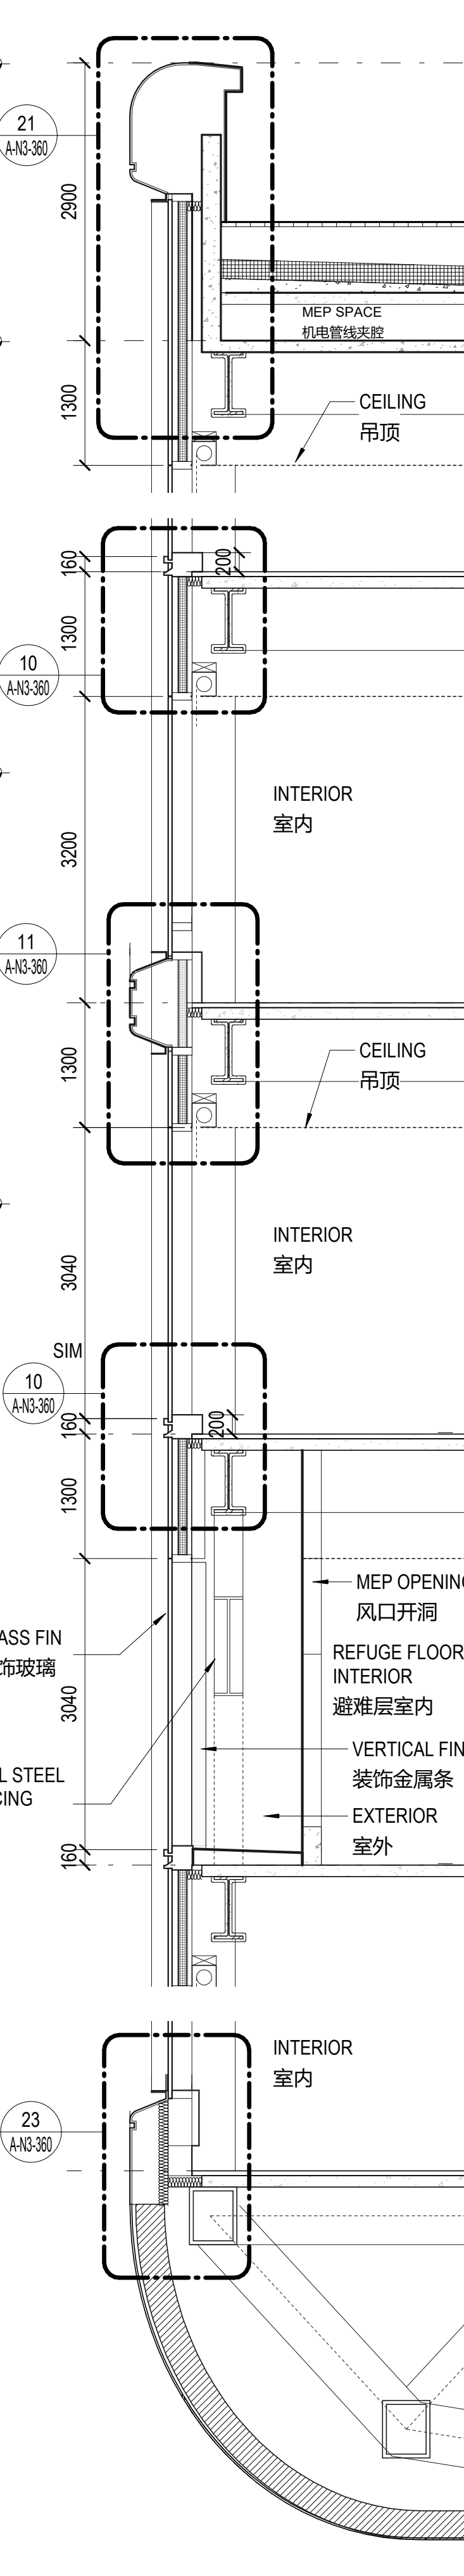

CW-1 ENLARGED SECTION - TYP.
CW-1放大剖面-标准层

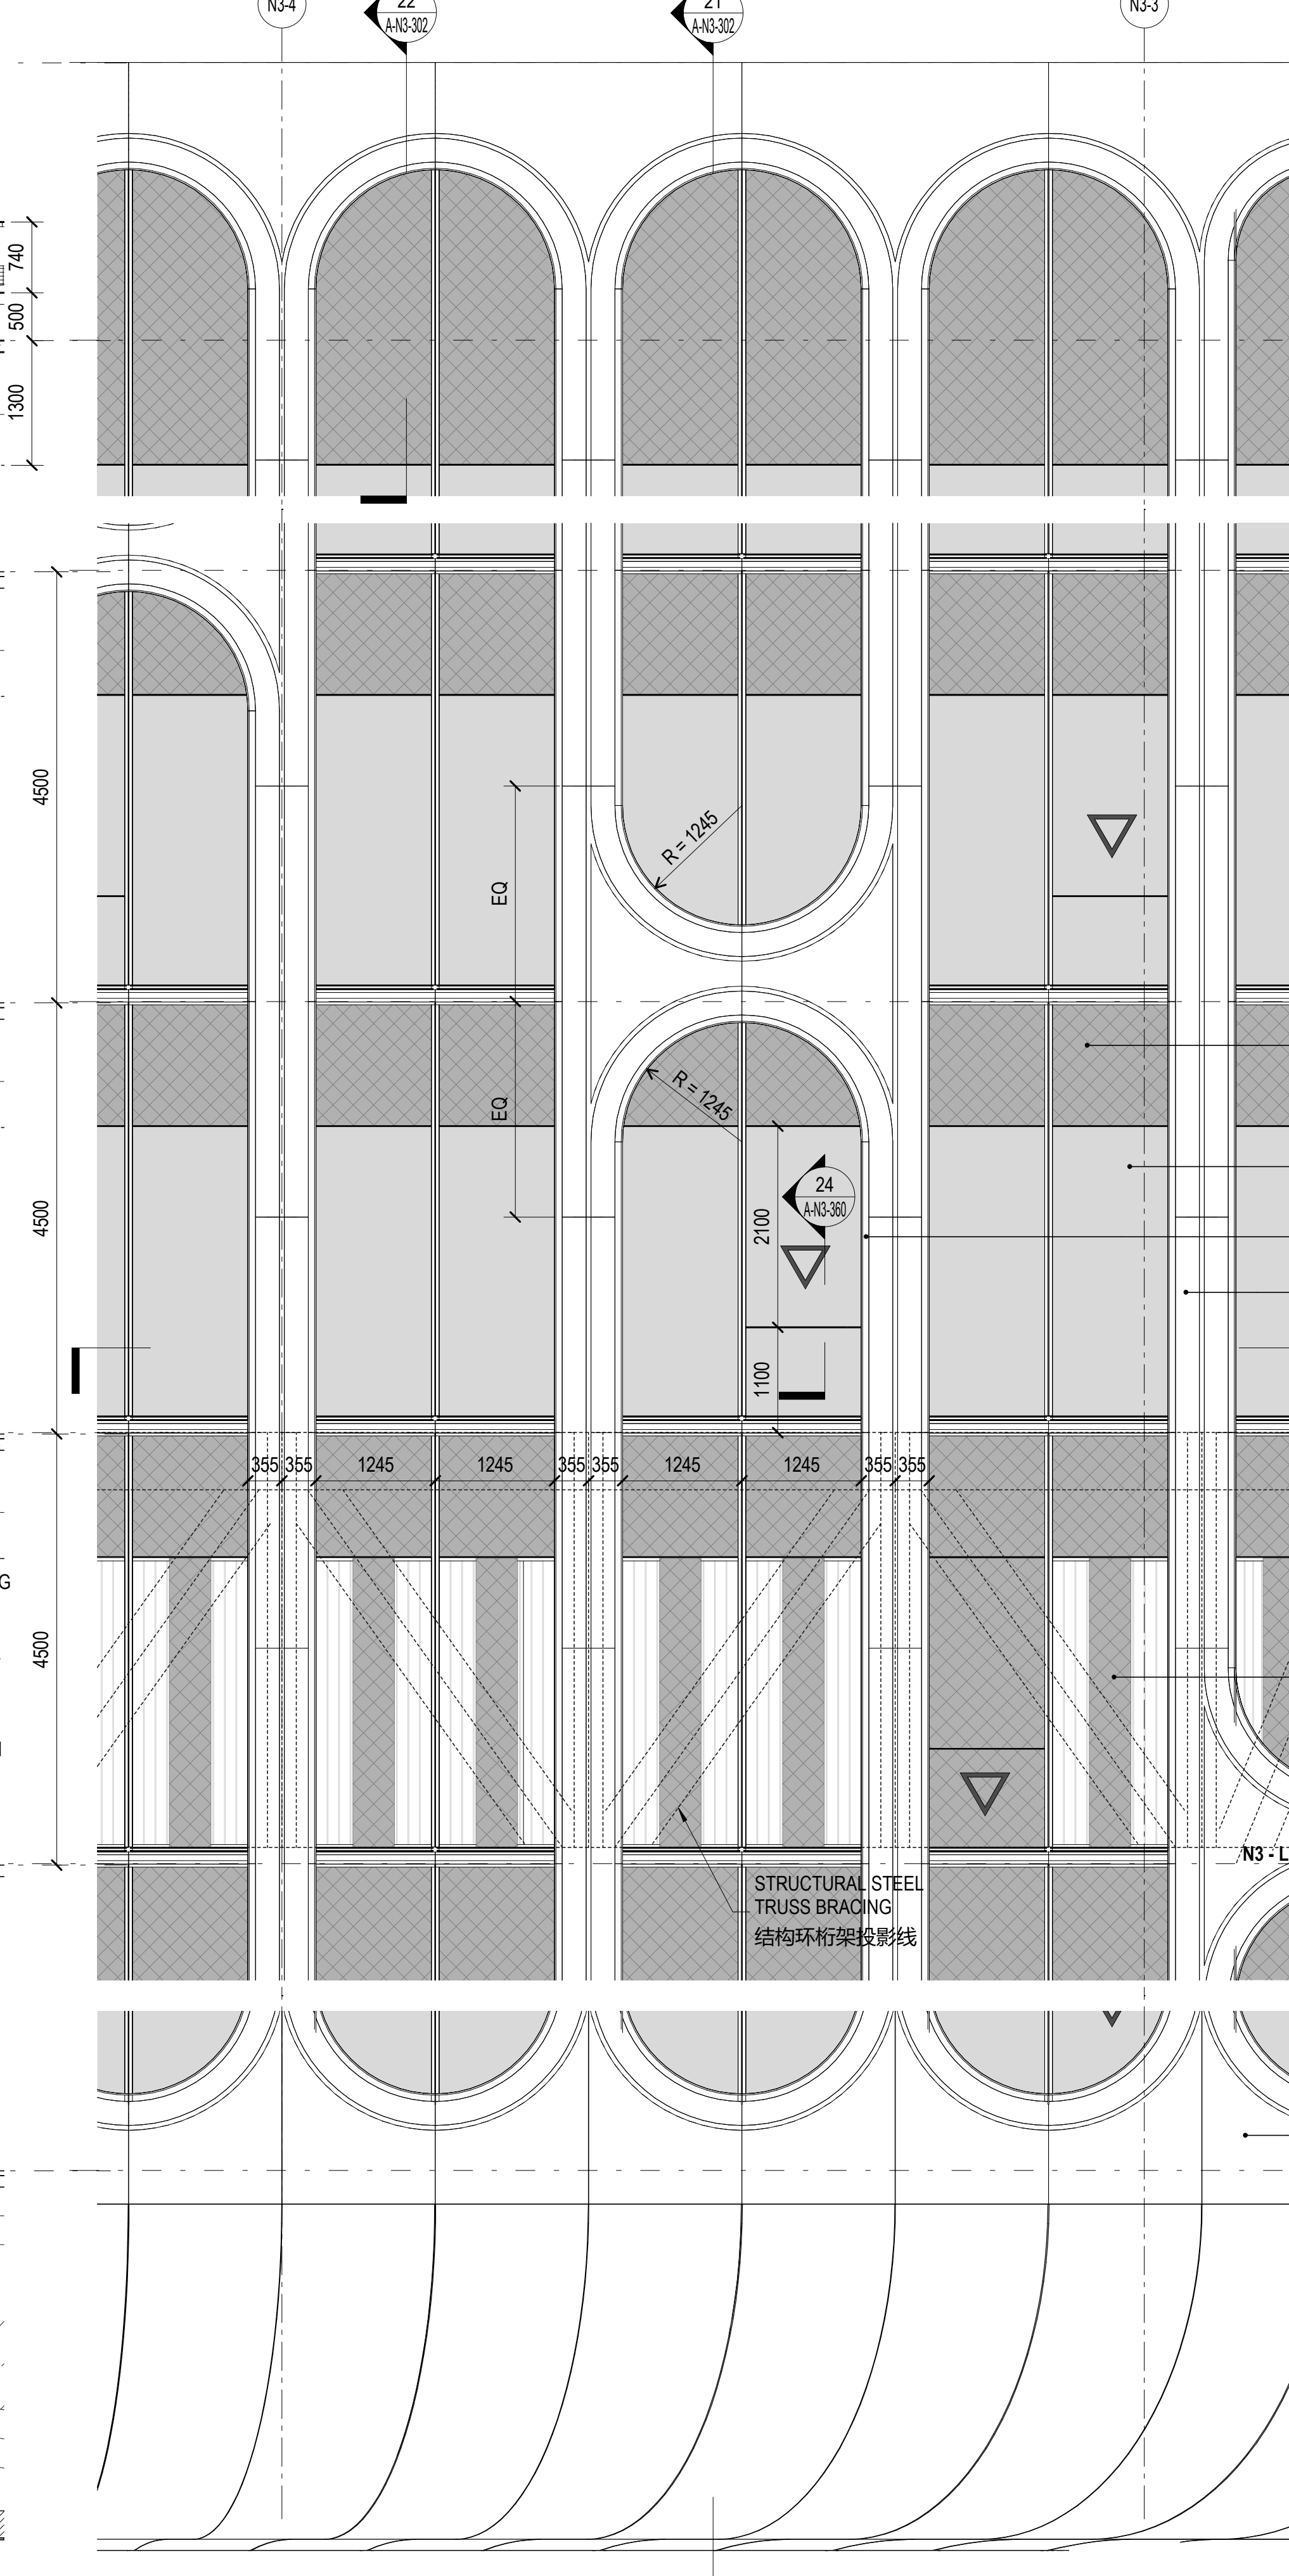

CW-1 ENLARGED ELEVATION
CW-1放大立面-标准段

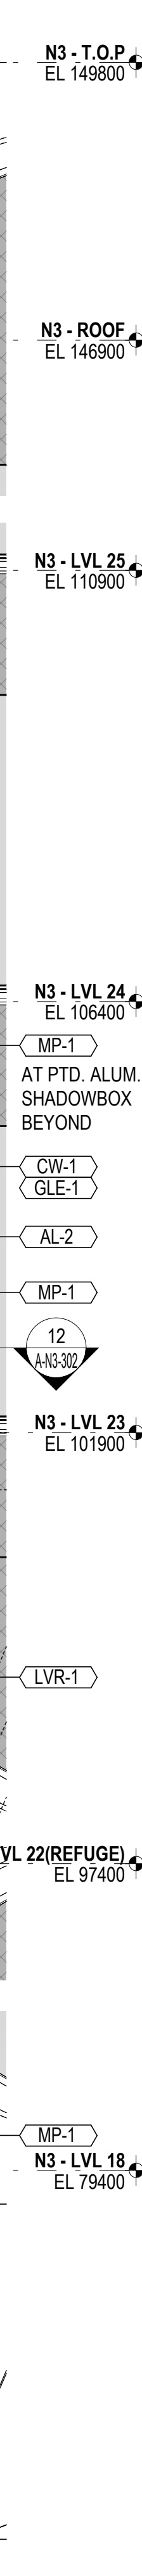

项目名称 Project Title

哔哩哔哩 新世代产业园 N3 地块

BiliBili SH HQ Plot N3

业主 Client
上海幻彼成实业有限公司

建筑设计 Architect
ENNEAD ARCHITECTS, LLP
1 World Trade Center 40th floor
New York, NY 10007
中国上海黄浦区建国中路10号
8号楼5号楼5205室

设计院 Design Institute
ECADI 华建集团华东建筑设计研究院
中国上海黄浦区中山南路1799号
世博浦江大厦北楼十八楼
18F North Tower Expo Binjiang Building,
1799 Zhongshan South Road,
Huang Pu District, Shanghai 200011 PRC

结构设计 STRUCTURE
奥雅纳 Arup
中国上海徐汇区淮海路1045号 (M)
淮海广场三十九楼
39F Huai Hai Plaza, 1045 Huai Hai Road (M)
Xu Hui District, Shanghai 200031 PRC

幕墙顾问 Façade Consultant
阿法建筑设计咨询 RFR
中国上海徐汇区汾阳路138号
轻科大厦四楼
4F QingKe Mansion, 138 Fen Yang Road
Xu Hui District, Shanghai 200031 PRC

灯光 LIGHTING
BPI
中国上海淮海东路99号十四楼K 室
Room K, 14F, NO.99 Huaihai East Rd,
Shanghai 200021 PRC

交通 TRANSPORTATION
MVA 弘达交通顾问有限公司
中国上海静安区天目西路218号
嘉里不夜城第一座2305室
Room 2305, Block 1, Jia Li Nocturnal City
No.218, Tianmu West Road, Shanghai PRC

Key Plan

比例 Scale
1 : 50

图纸名称 Sheet Title
N3- CW-1 SYSTEM DRAWINGS
建筑N3塔楼CW-1主立面外墙系统

图纸编号 Sheet No.
A-N3-302