


上海临港新片区
金融总部湾区
首发项目
15-01地块
Shanghai Lingang
Free Trade Zone
New Area Financial
Headquarters Zone
Plot 15-01

业主 Client
上海临港经济发展（集团）有限公司
Shanghai Lingang Economic
Development Group Co., Ltd.

建筑设计 Architect
ENNEAD ARCHITECTS, LLP
1 World Trade Center 40th floor
New York, NY 10007
212.807.7171 tel 212.807.5917 fax
www.ennead.com

设计院 Design Institute
华东建筑设计研究院有限公司
华东都市建筑设计研究总院
上海市恒丰路329号 中港汇·静安19
楼
East China Architectural Design &
Research Institute Co.,Ltd
East China Urban Architectural Design &
Research Institute
19F, NO.329 Hengfeng Road,
Shanghai, China
www.udud.cn

幕墙顾问 Façade Consultant
阿法建筑设计咨询（上海）有限公司
上海市徐汇区汾阳路138号轻科大
厦四层
RFR Shanghai
138 Feng Yang Road, Shanghai
Tel 电话: +86 021 54665316
Fax 传真: +86 021 54665317

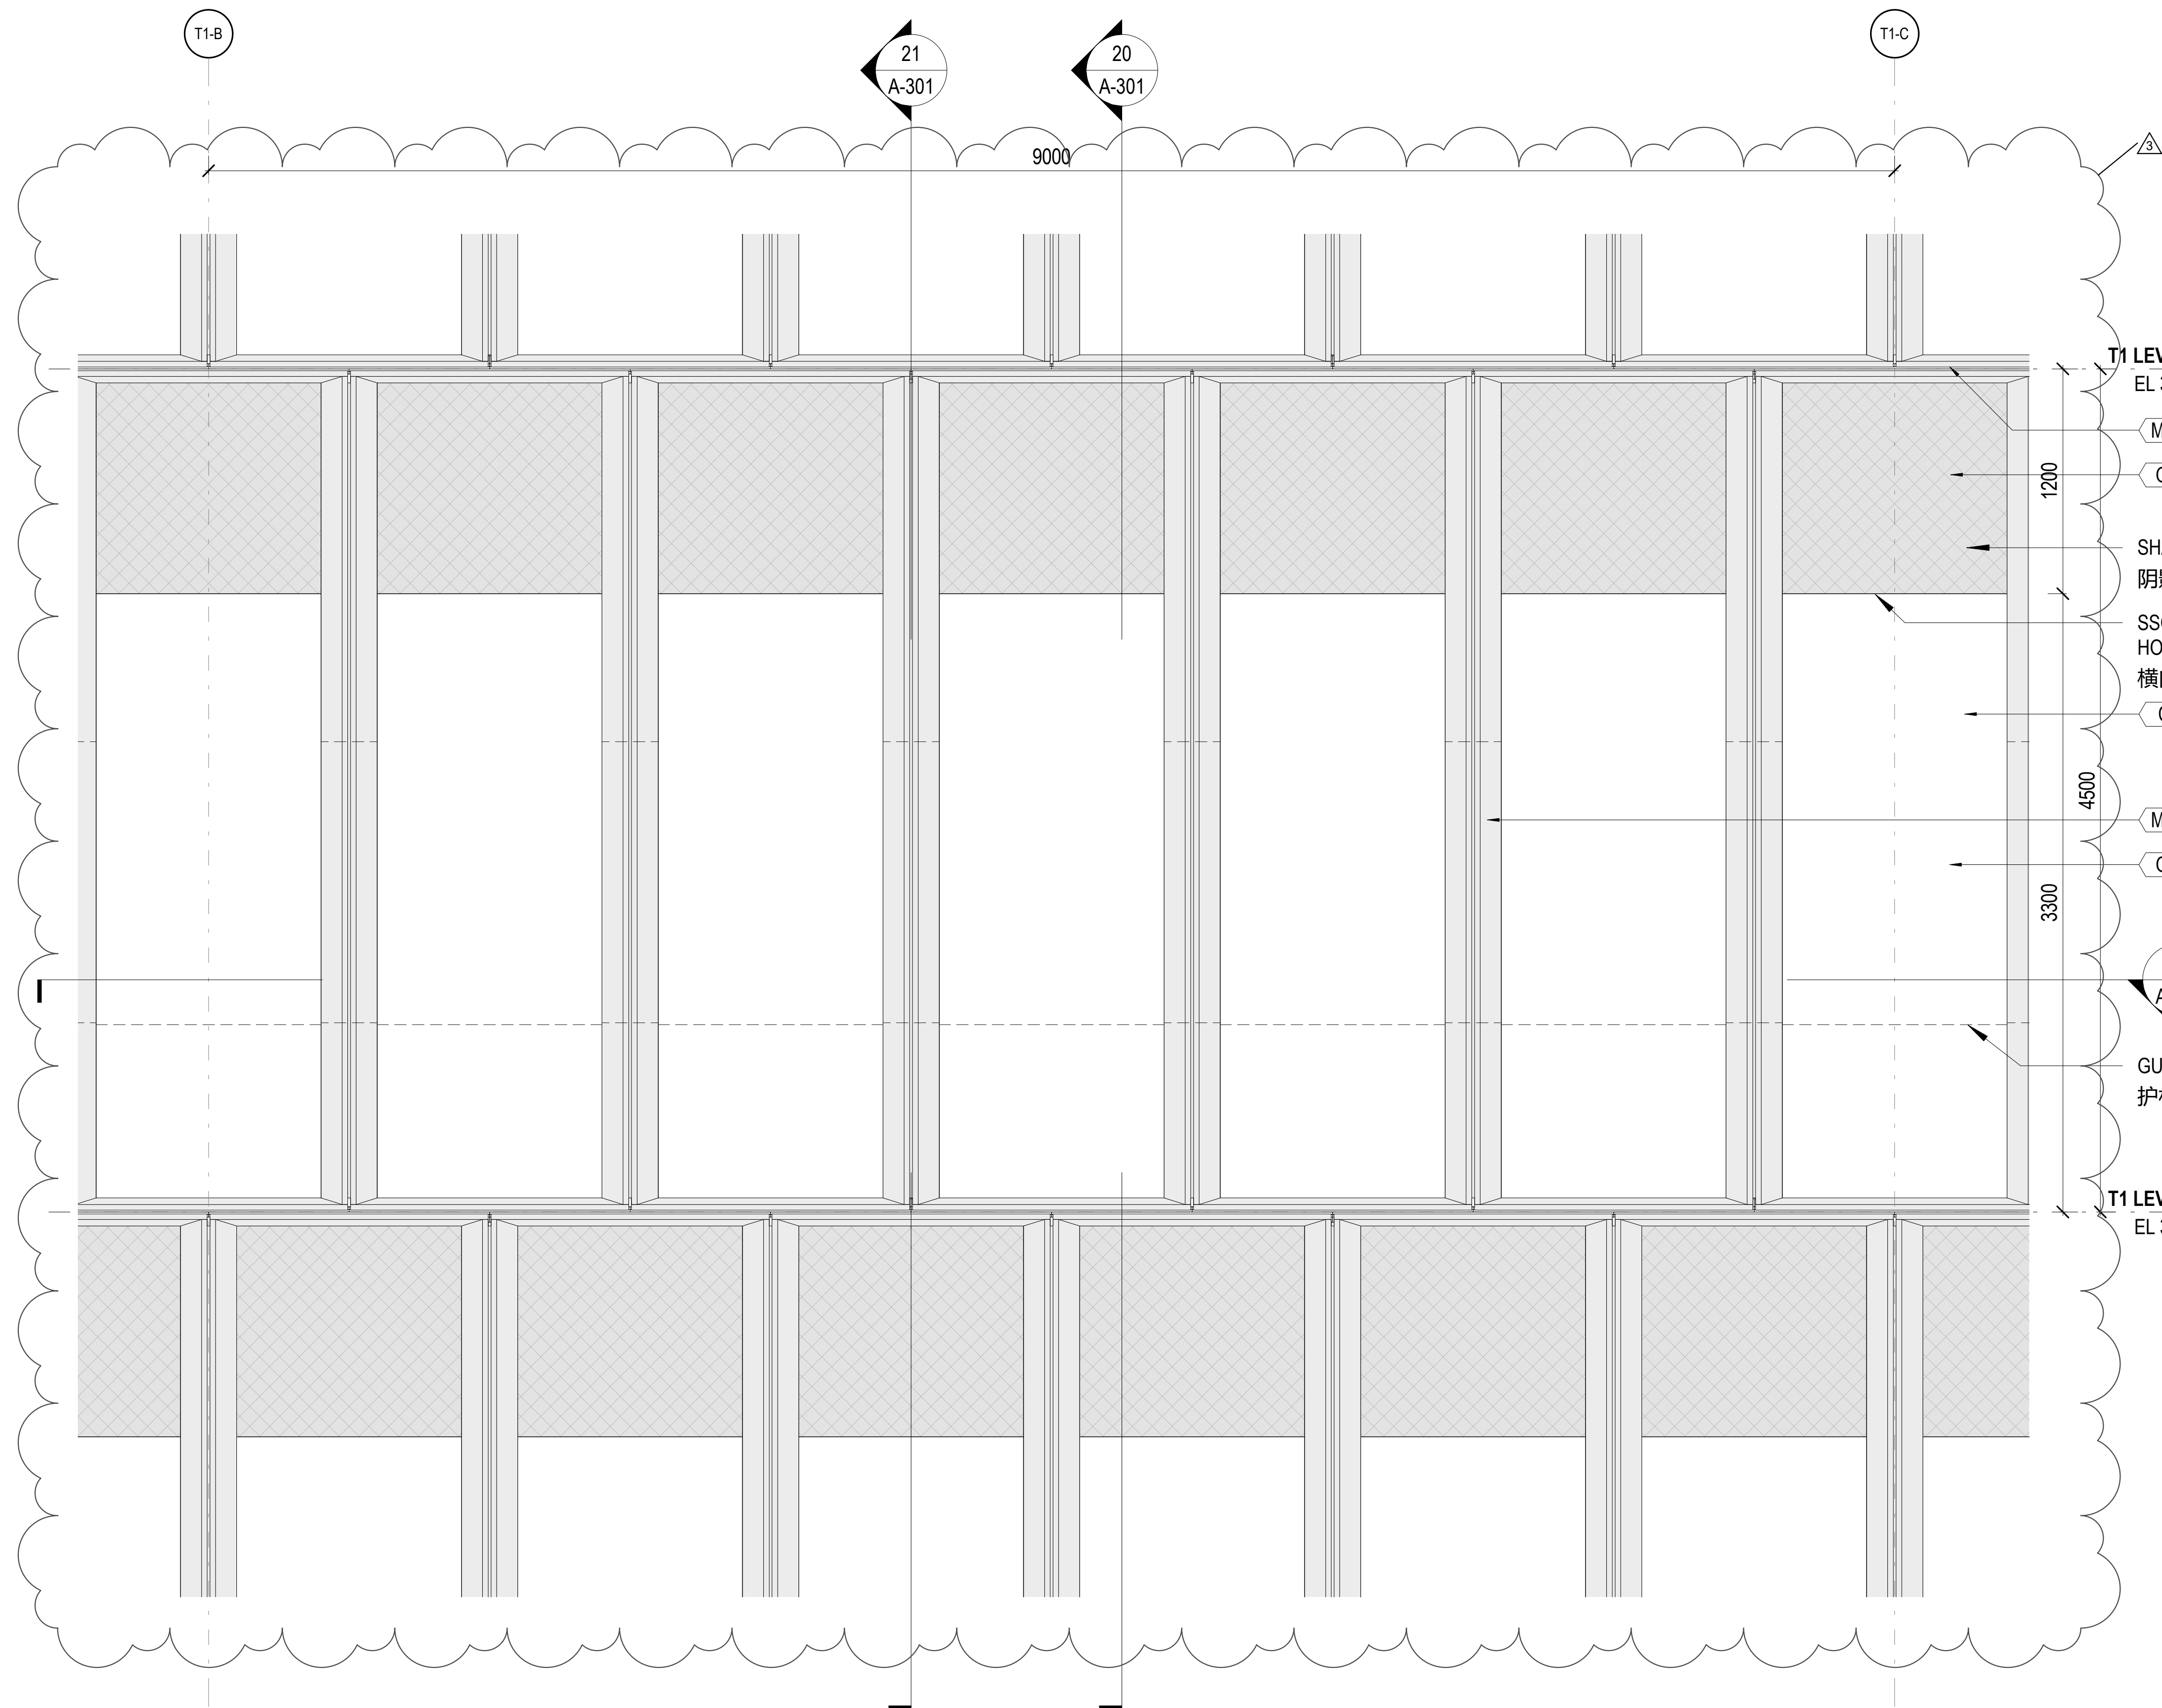


23 TOWER CW (CW-1)- ELEVATION
T1号楼典型幕墙(CW-1)-立面
1 : 20


22 TOWER CW (CW-1)- OPERABLE WINDOW ELEVATION
T1号楼典型幕墙(CW-1)开启窗立面图
1 : 20

21 TOWER CW (CW-1)- OPERABLE WINDOW
T1号楼典型幕墙(CW-1)-剖面图2
1 : 20

20 TOWER CW (CW-1)- VISION GLASS
T1号楼典型幕墙(CW-1)-剖面图1
1 : 20

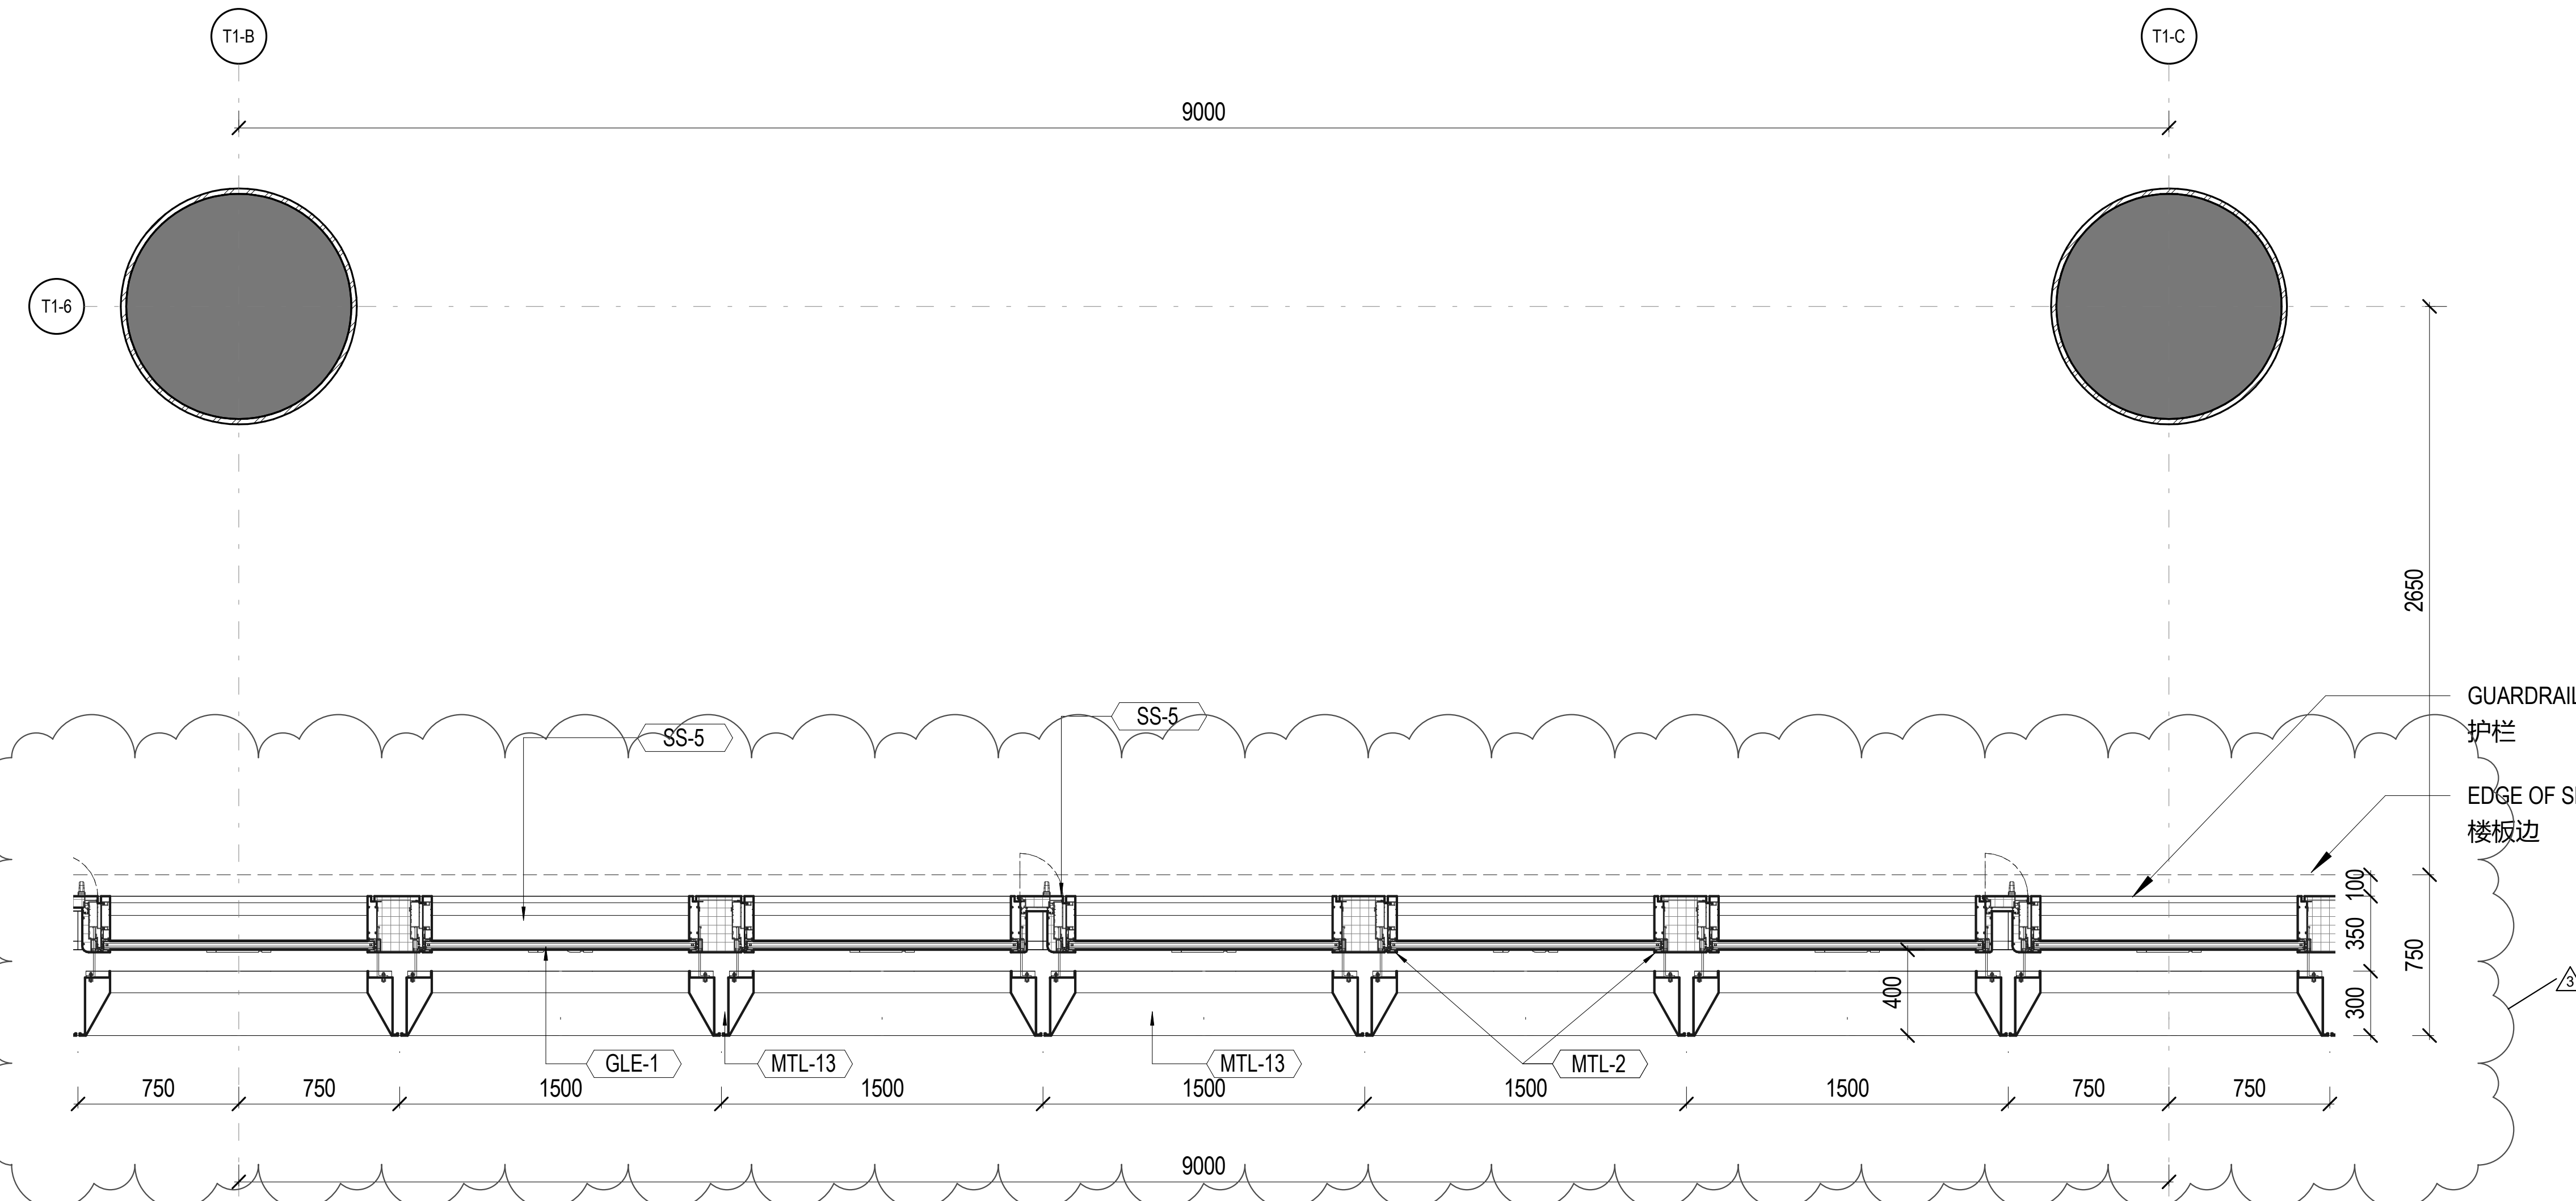


11 TOWER CW (CW-1) - PLAN
T1号楼典型幕墙(CW-1)-平面
1 : 20

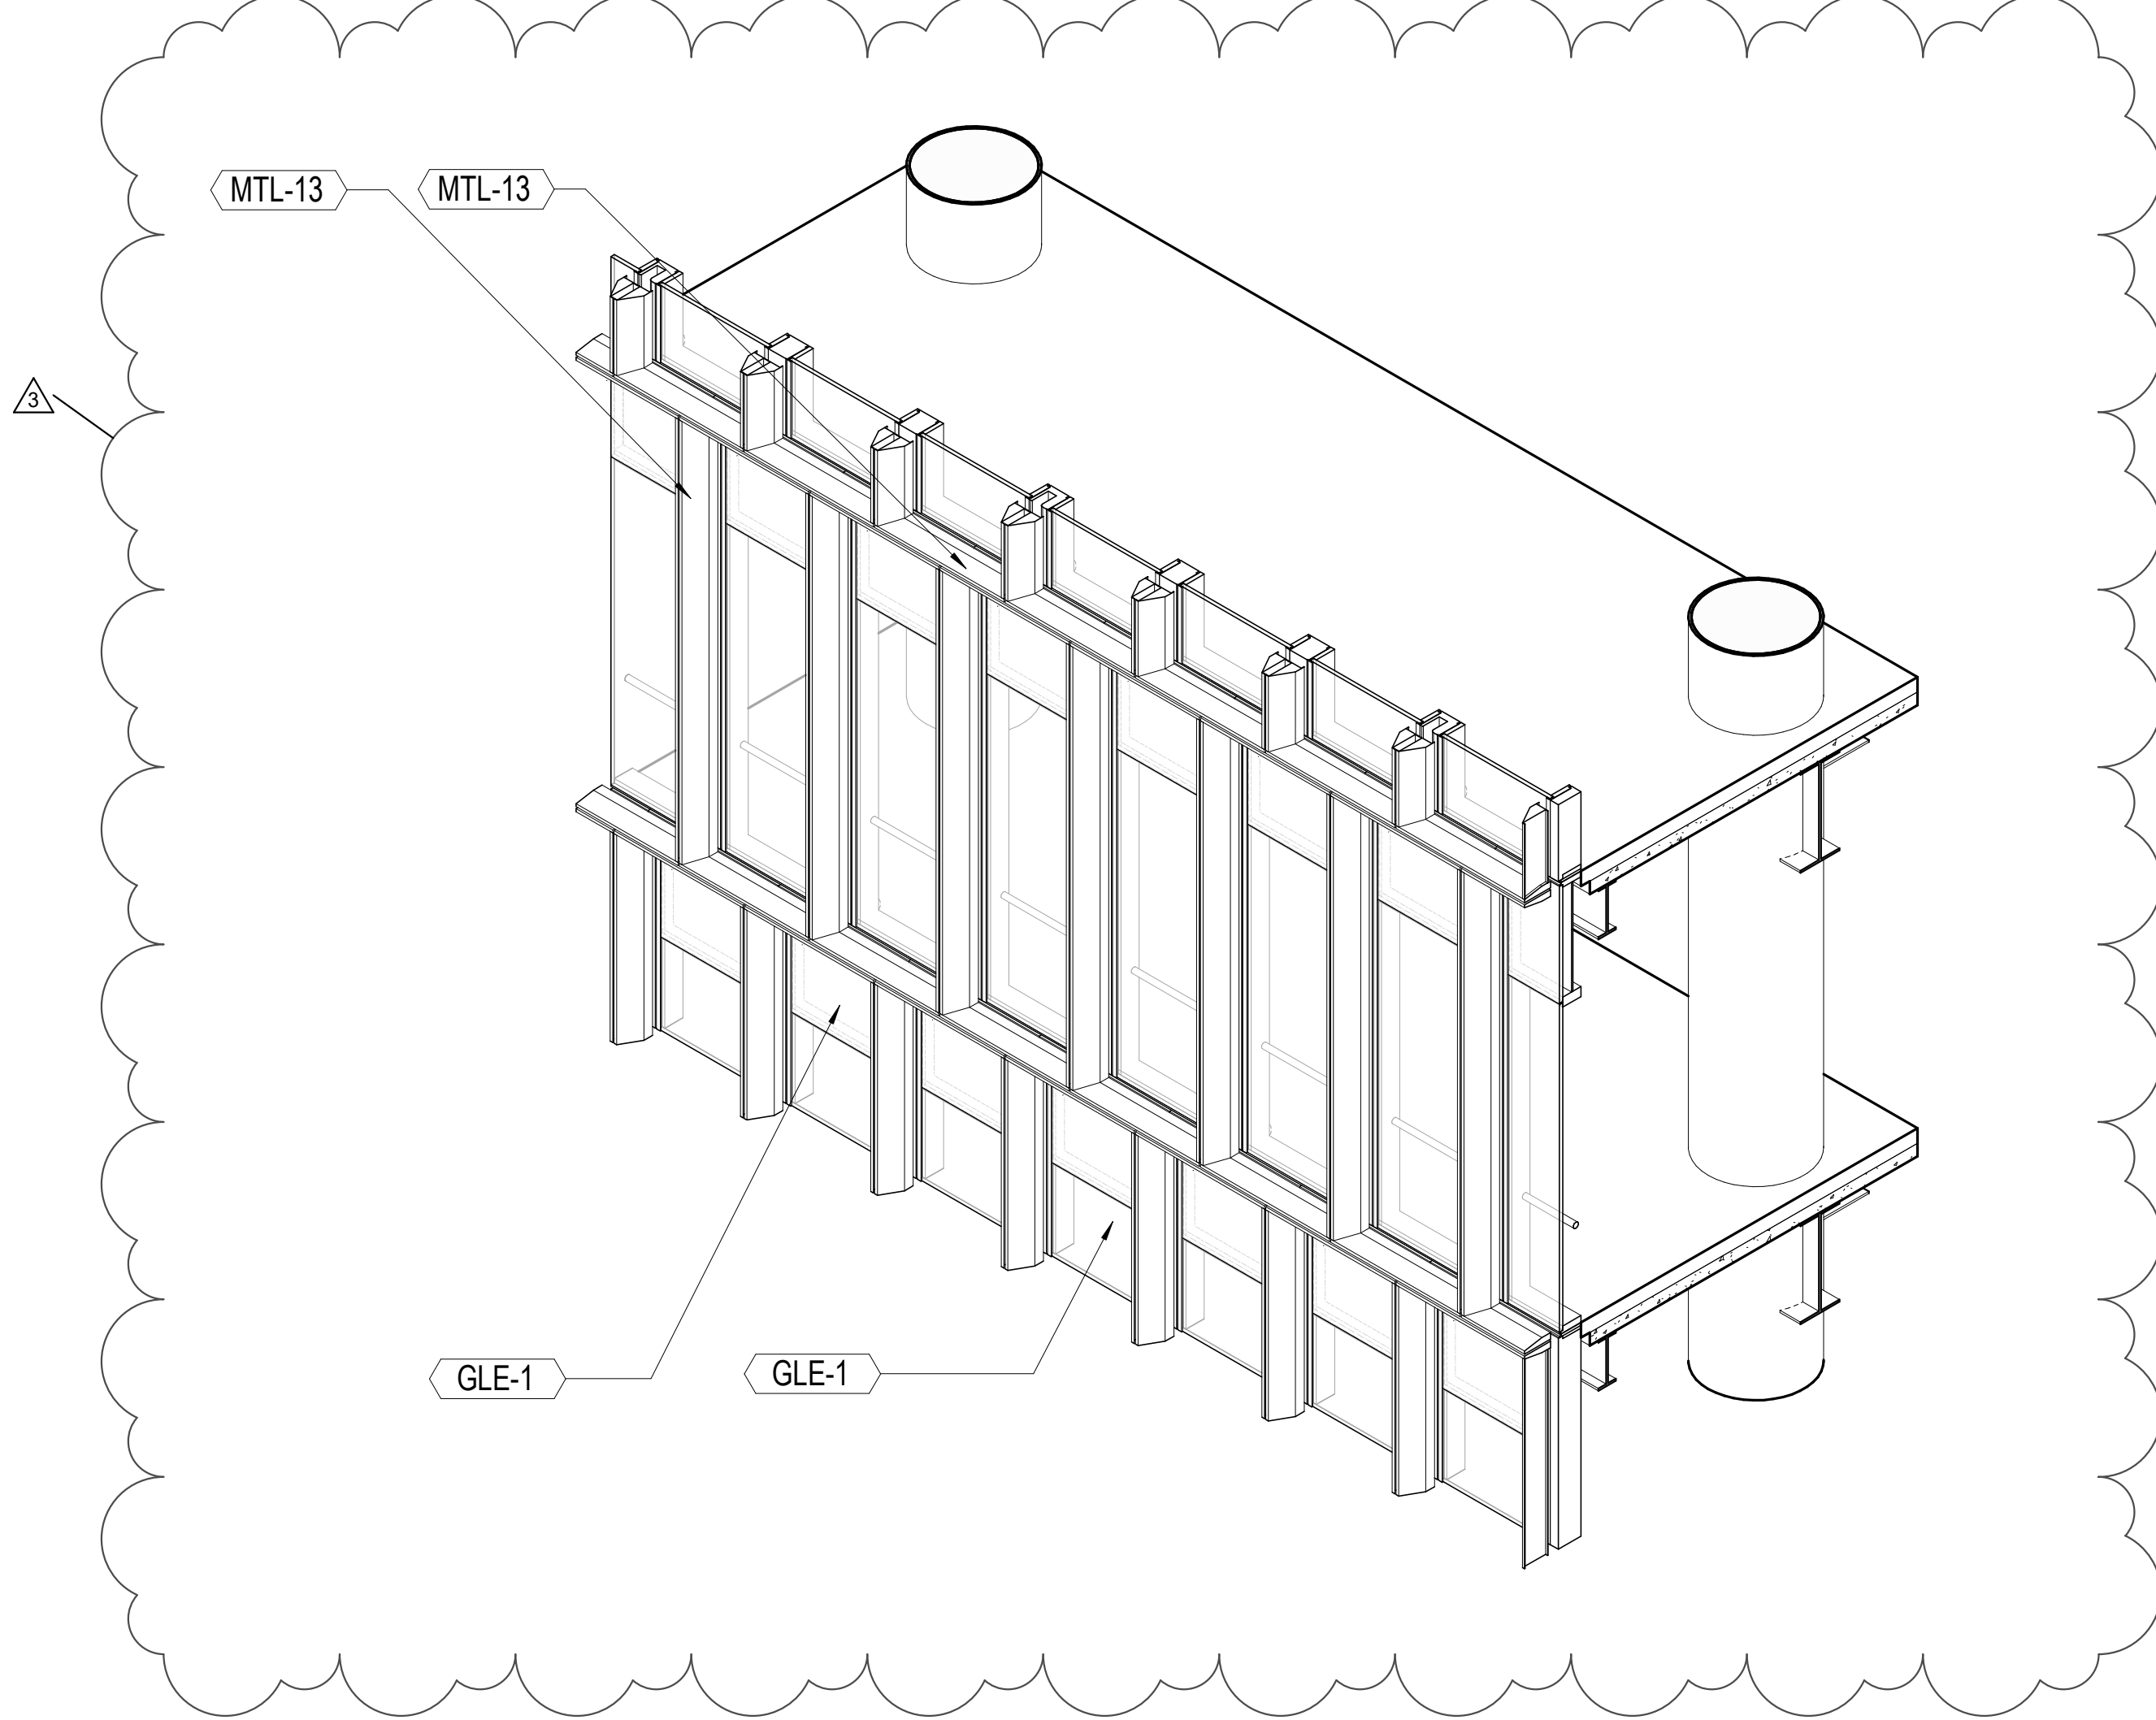

10 TOWER CW-1 TYPICAL - AXON
T1号楼塔楼典型幕墙(CW-1)-轴测图

Seal

Key Plan

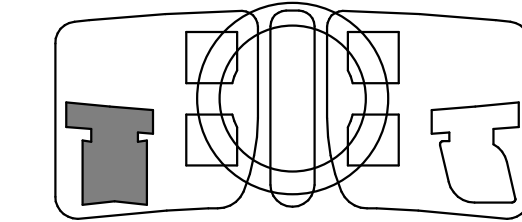

3	CW ISSUE REVISION 2	2021/07/07
2	100% CURTAIN WALL GD ISSUE	2021/03/31
1	PROGRESS CW GD ISSUE	2021/01/15
No.	Issue Name	Date

日期 Date
2021-03-31
项目号 Project Number
1940
比例 Scale
1 : 20

图纸名称 Sheet Title
塔楼典型幕墙(CW-1)节点
TOWER CW (CW-1)

图纸标号 Sheet No.
A-301